




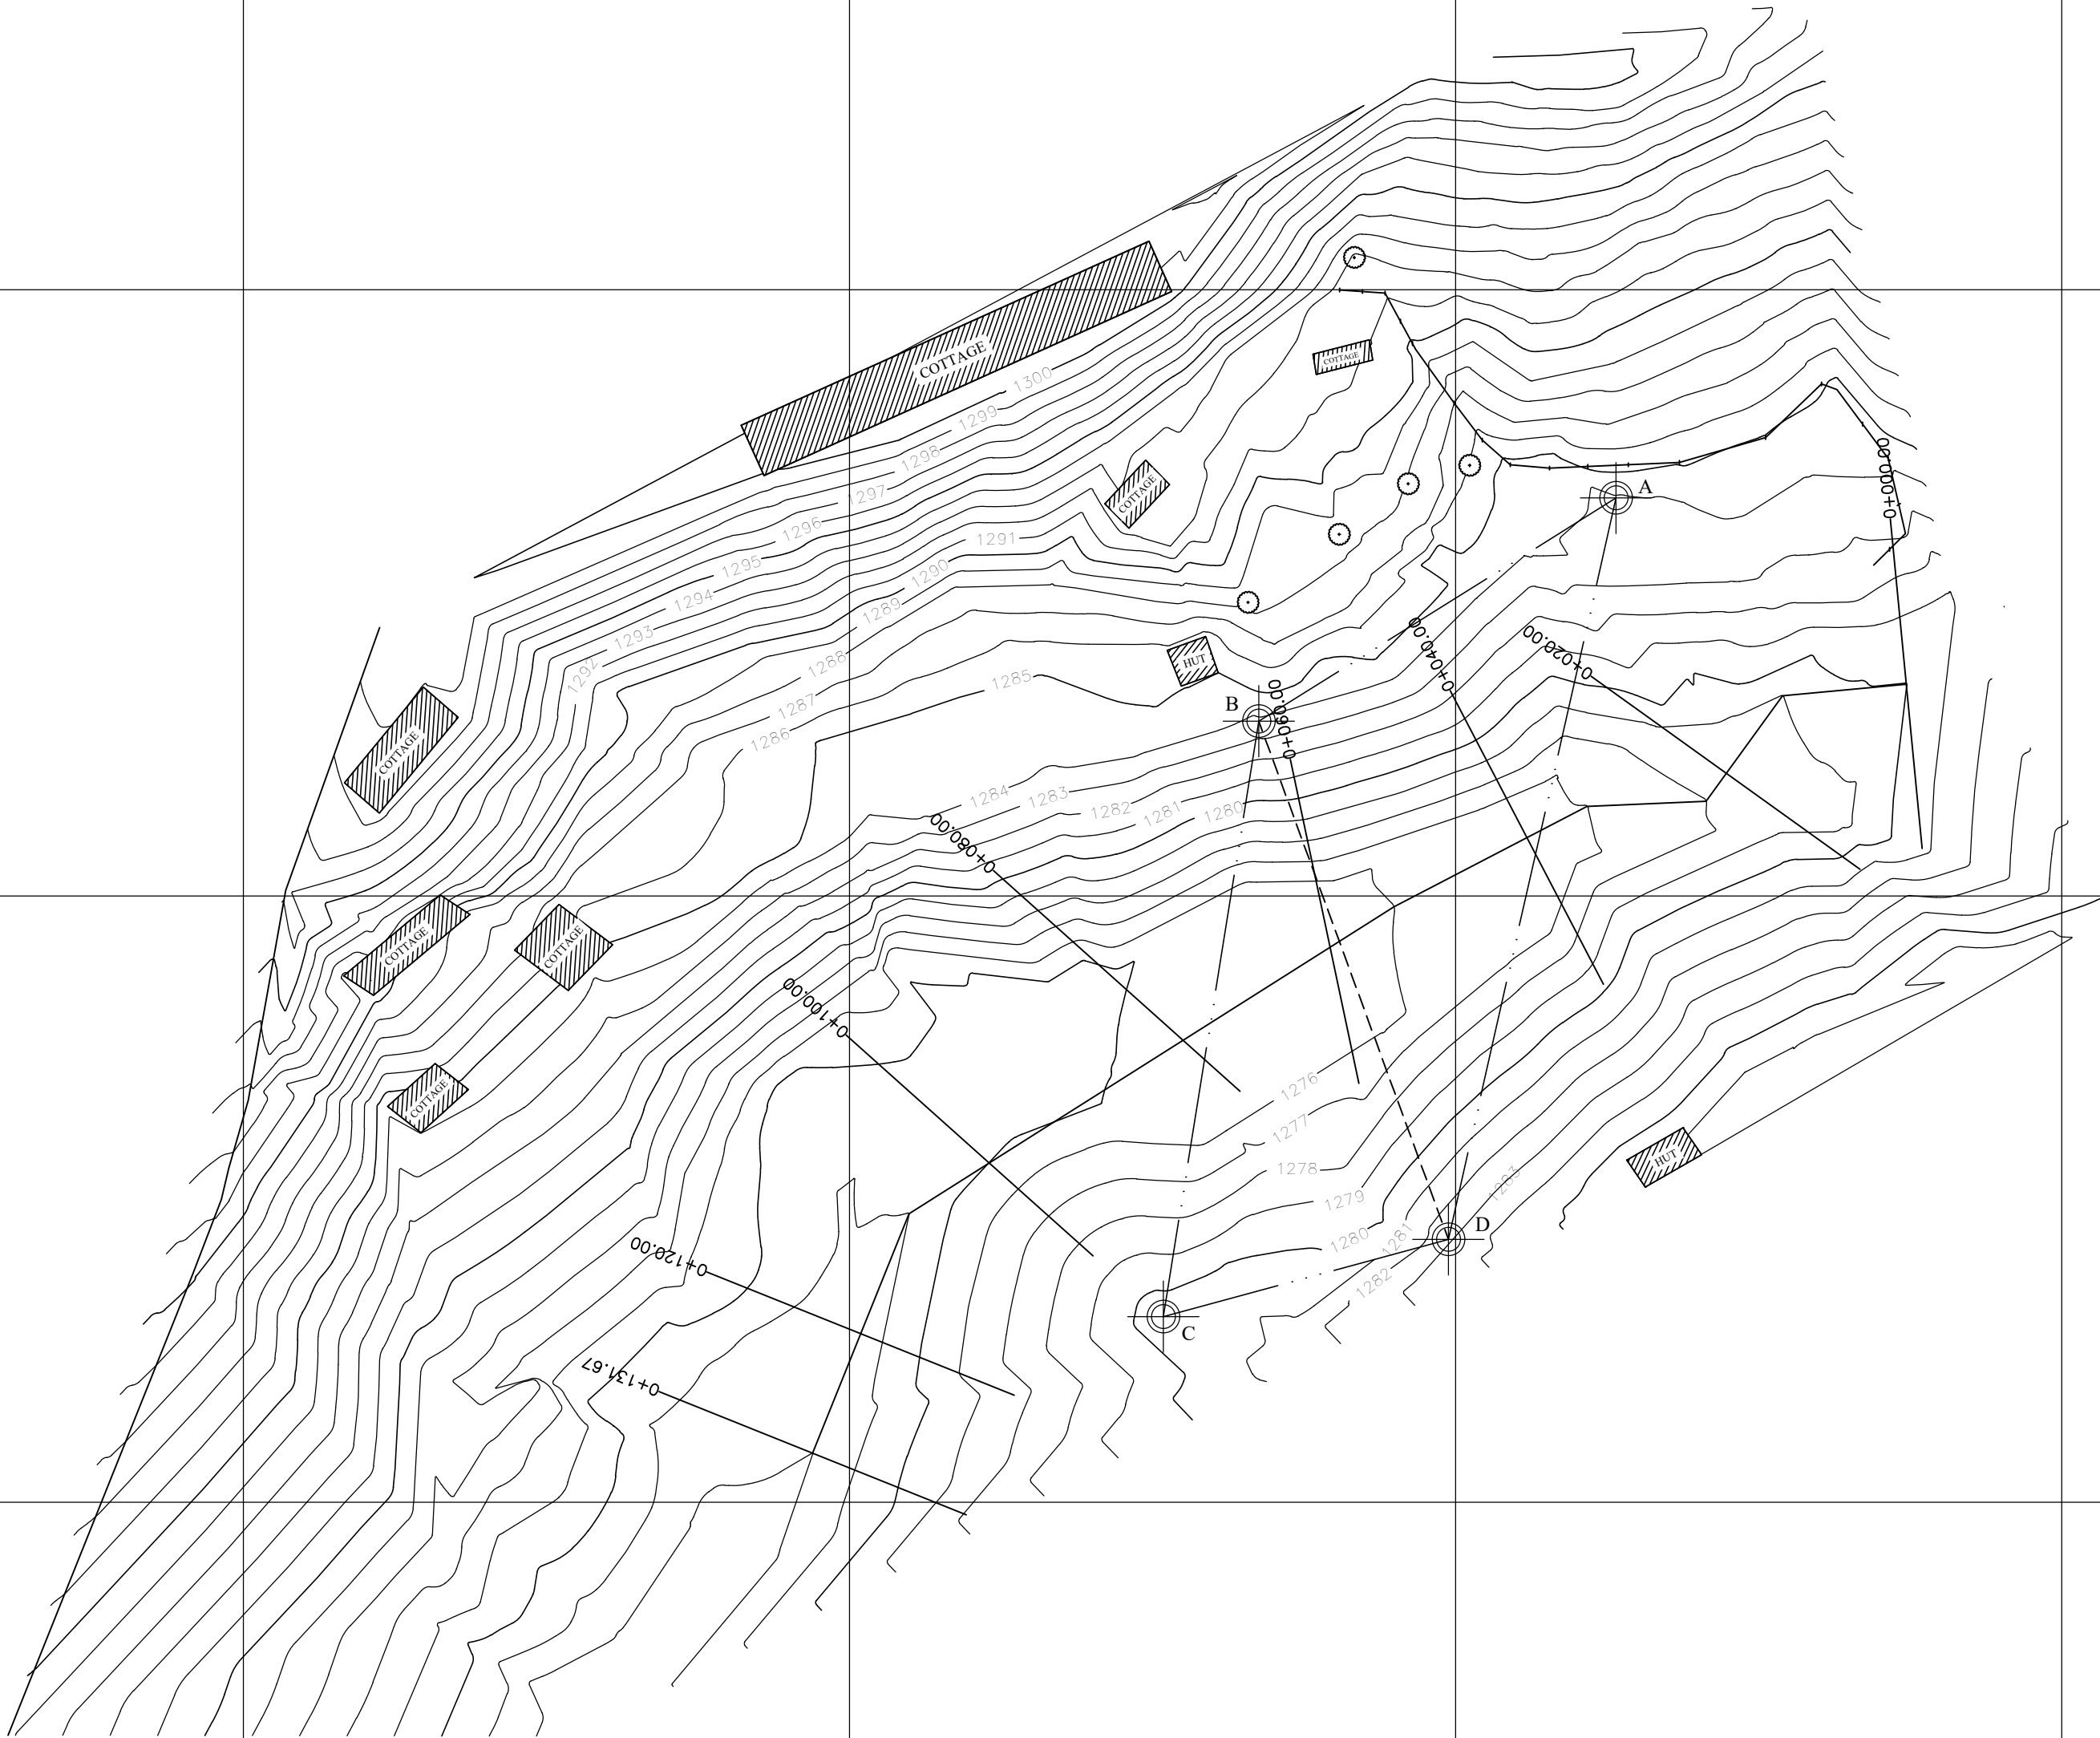

PLAN

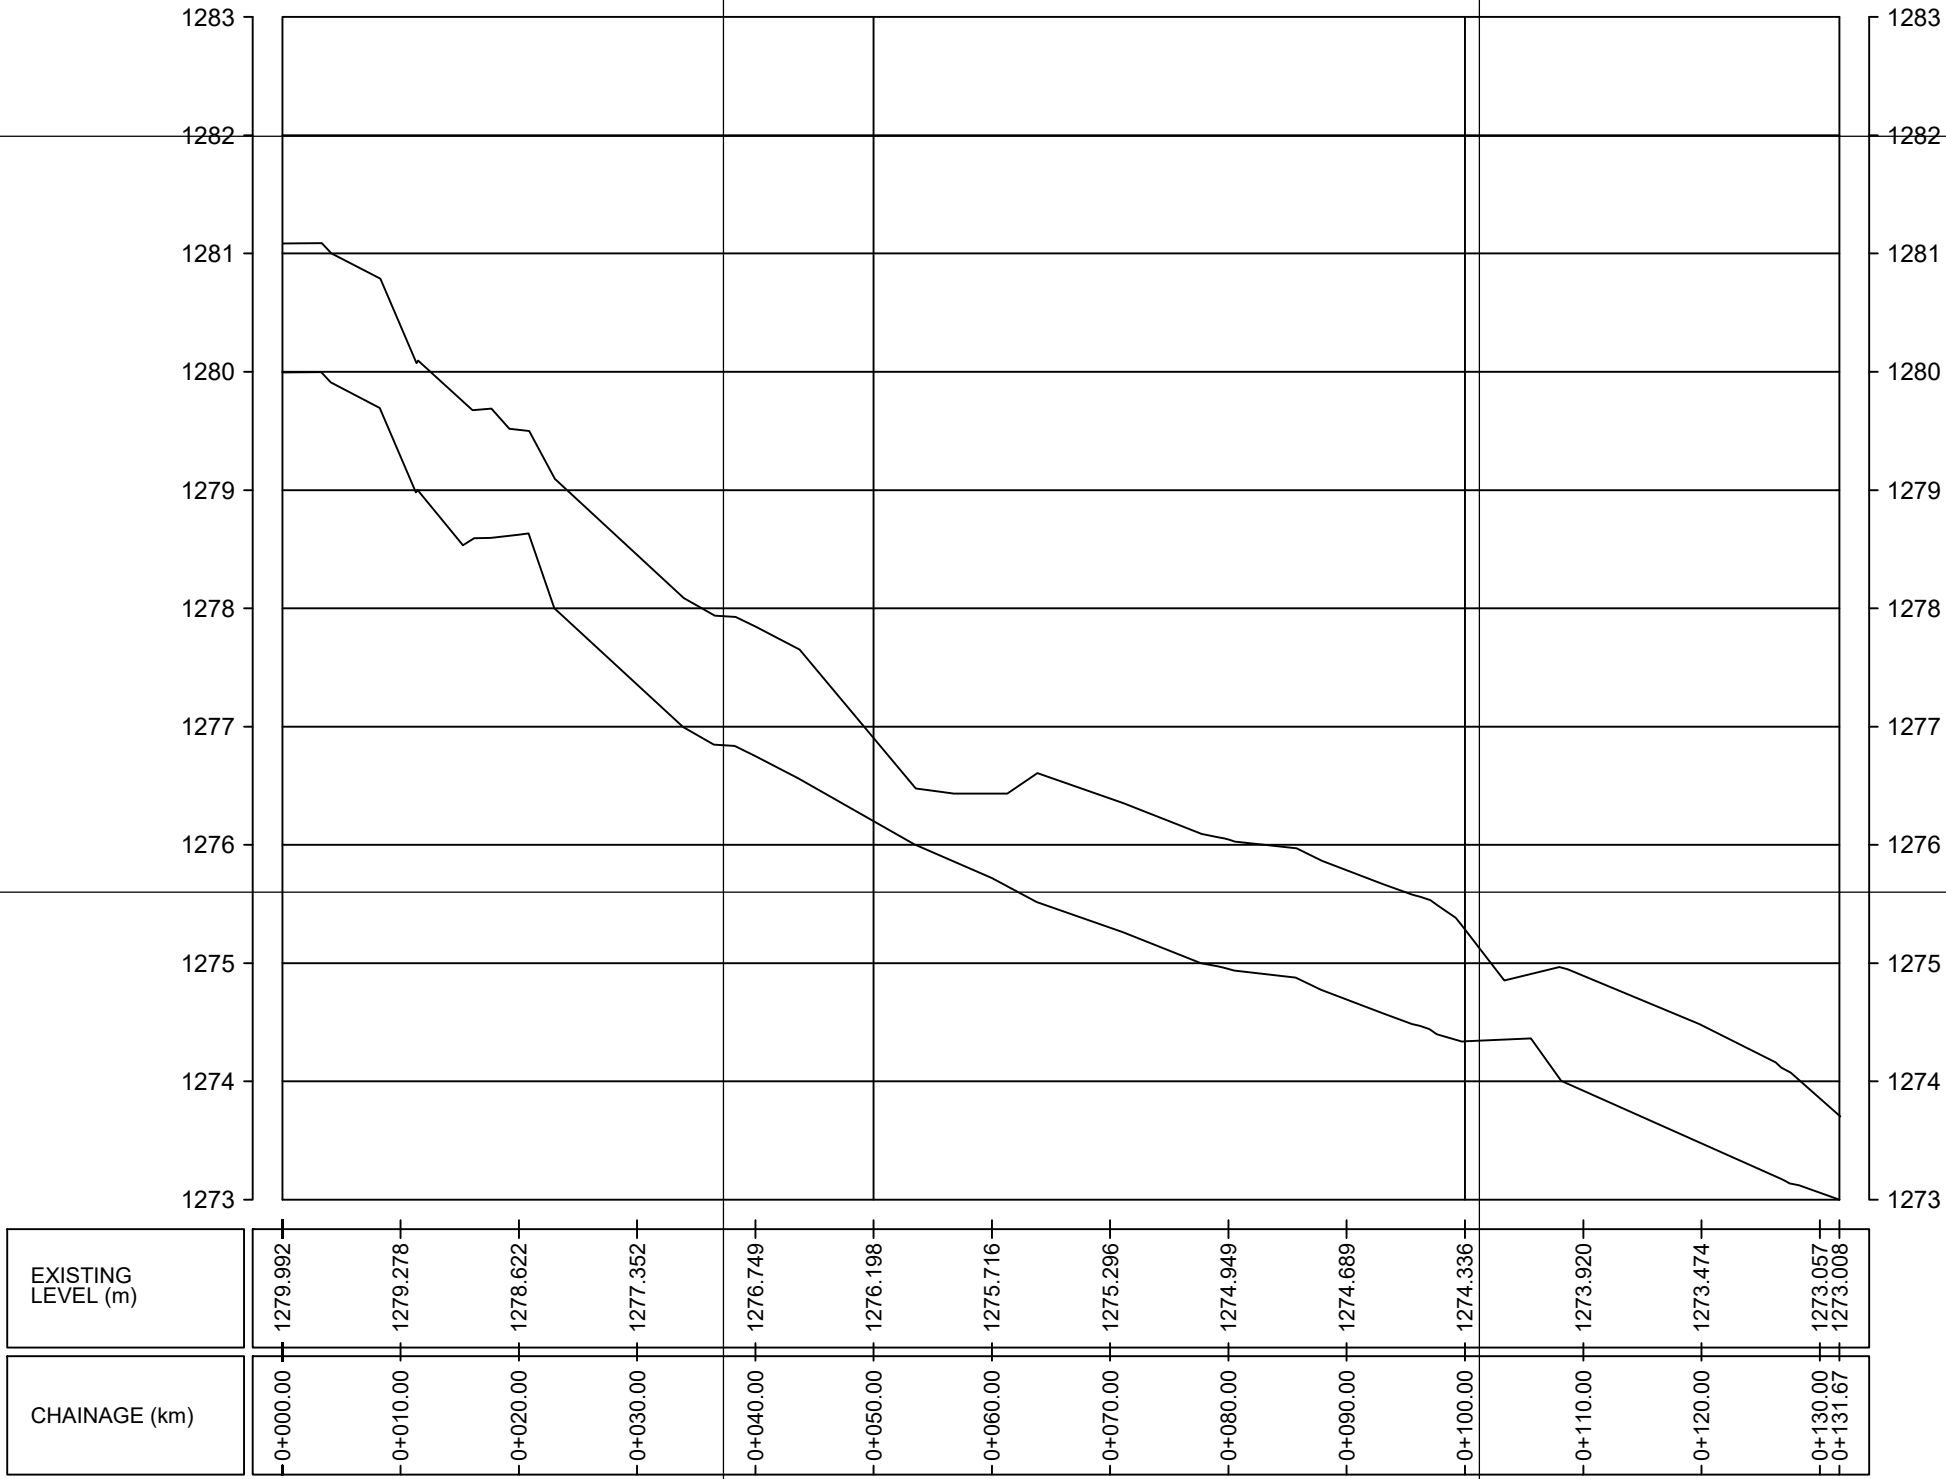

L-SECTION

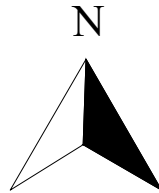

STN	NORTHING	EASTING	RL
A	3055837.806	332131.395	1283.888
B	3055817.584	332099.017	1283.856
C	3055763.651	332090.371	1280.102
D	3055770.640	332116.200	1282.264
TBM	3055820.792	3055820.792	1283.888

S.N.	LEGENDS	SYMBOL
1	NFL	————
2	BRIDGE AXIS	-----
3	WATER LEVEL	
4	GROUND	
5	AXIS LINE	

LOCATION: MARS NEPAL ENGINEERING
SURVEY CAMP, BUNGAMATI, LALITPUR

- BRIDGE SURVEYING
- 1.TOPOGRAPHICAL MAP
 2. LONGITUDINAL SECTION

SUBMITTED BY: GROUP 7
SAMBHAV BELBASE (5)
NILESH JHA (16)
NISHAN LUITEL (21)
ANSHU RAJ OLI (30)
SWAPNIL REGMI (38)
BIBEK KUMAR SHAH (40)

SUBMITTED TO:
DEPARTMENT OF CIVIL ENGINEERING
KATHMANDU UNIVERSITY

SHEET NO: 2

1. SCALE: 1:400

