
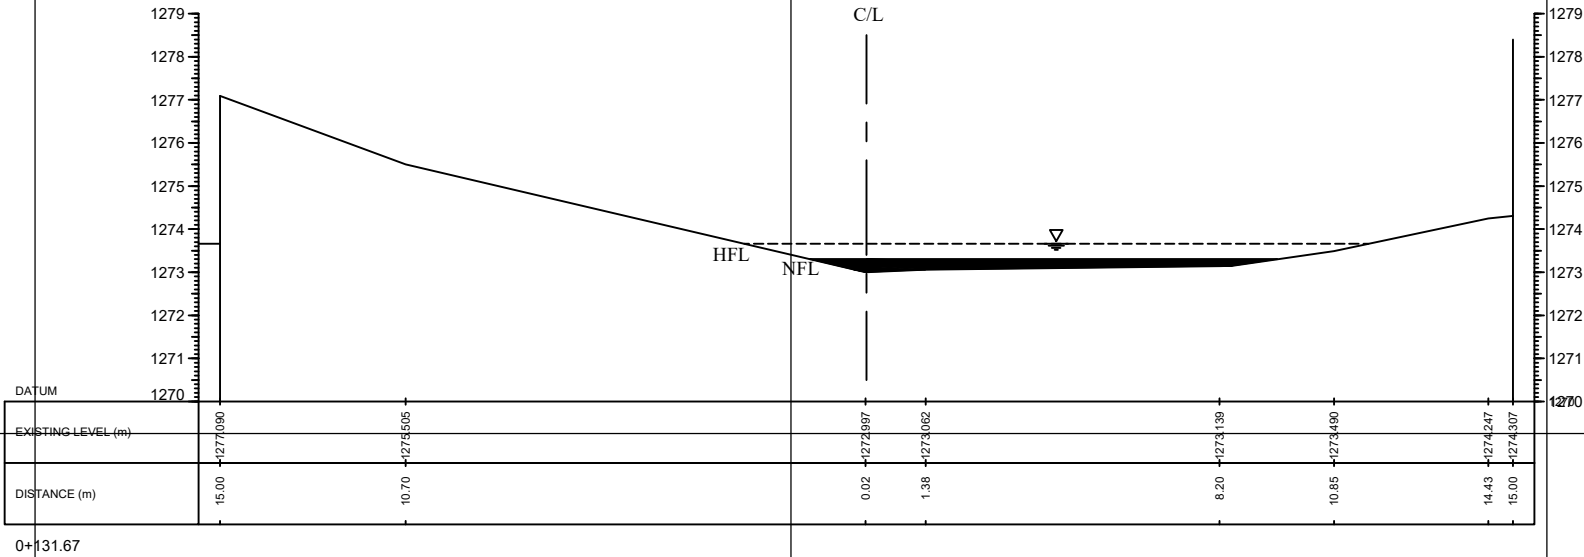
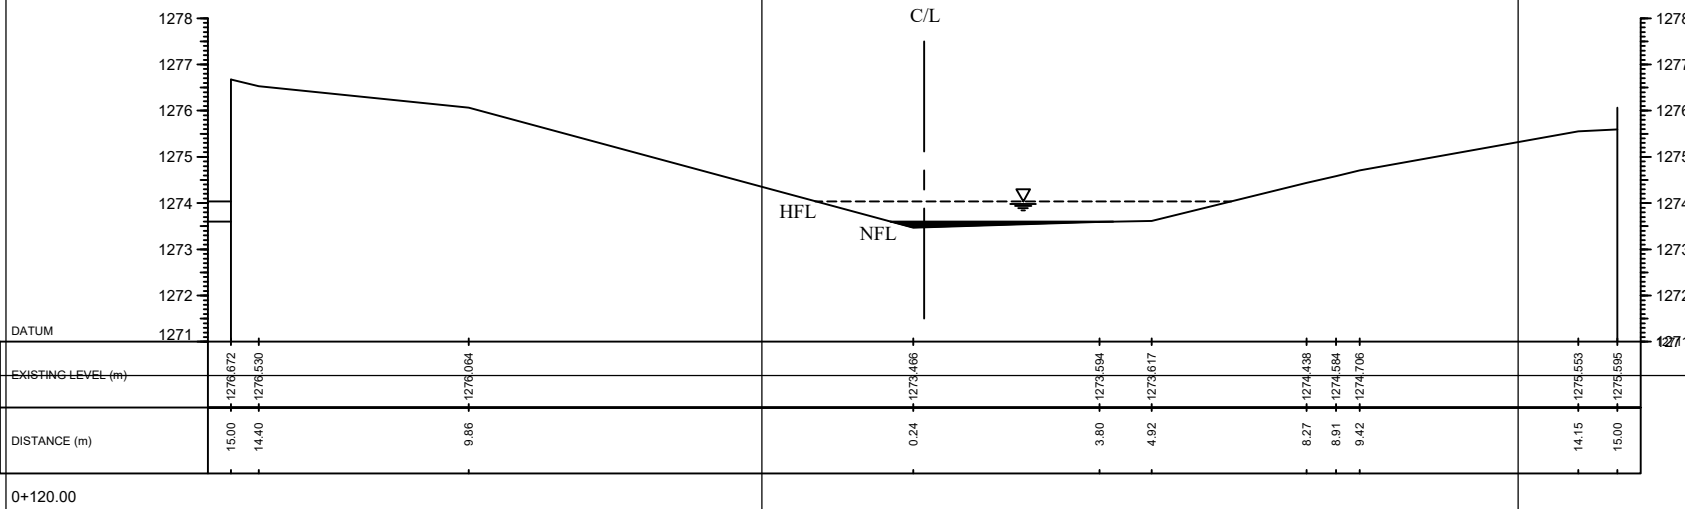
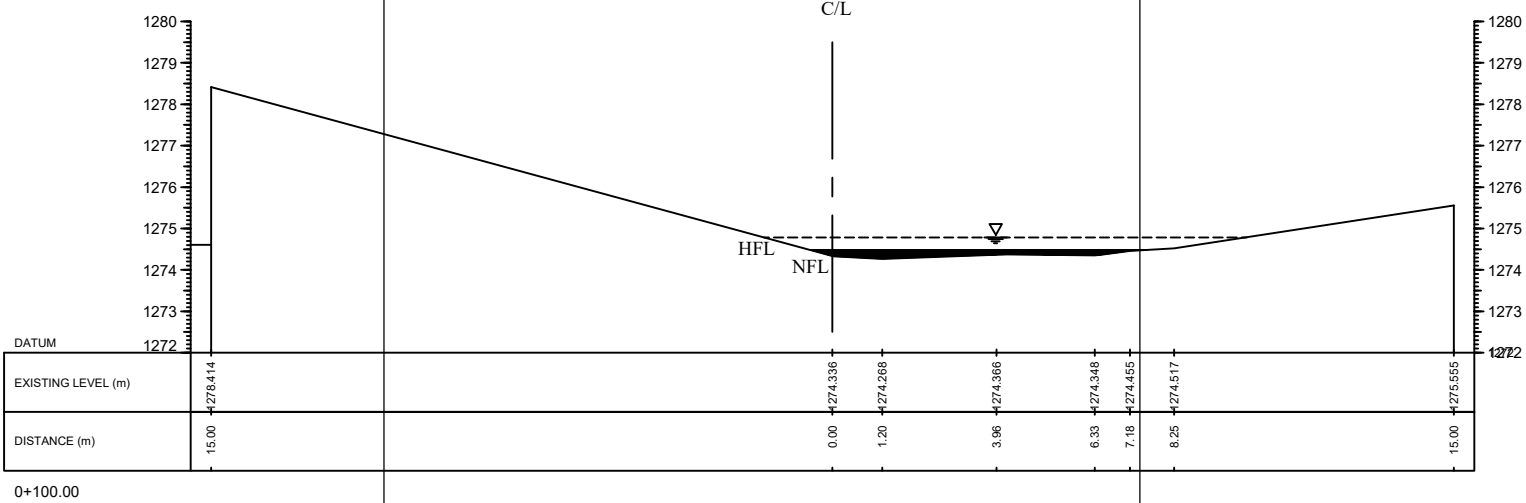
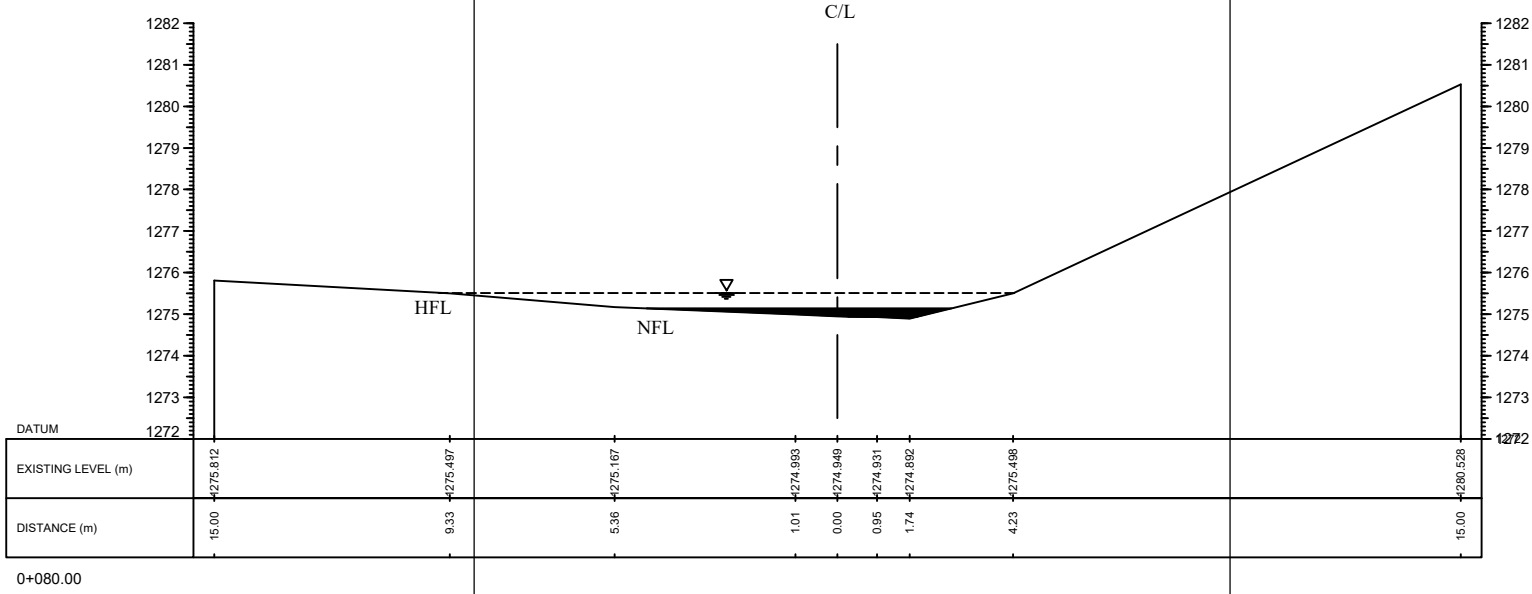
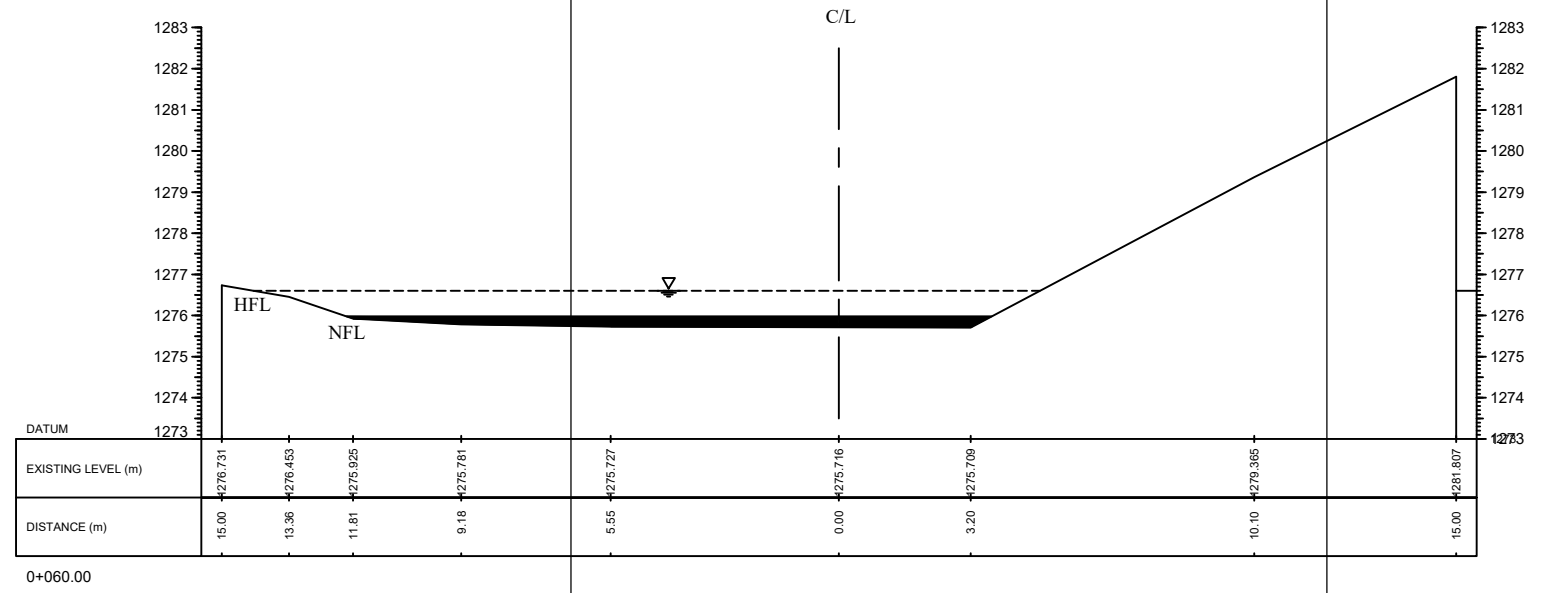
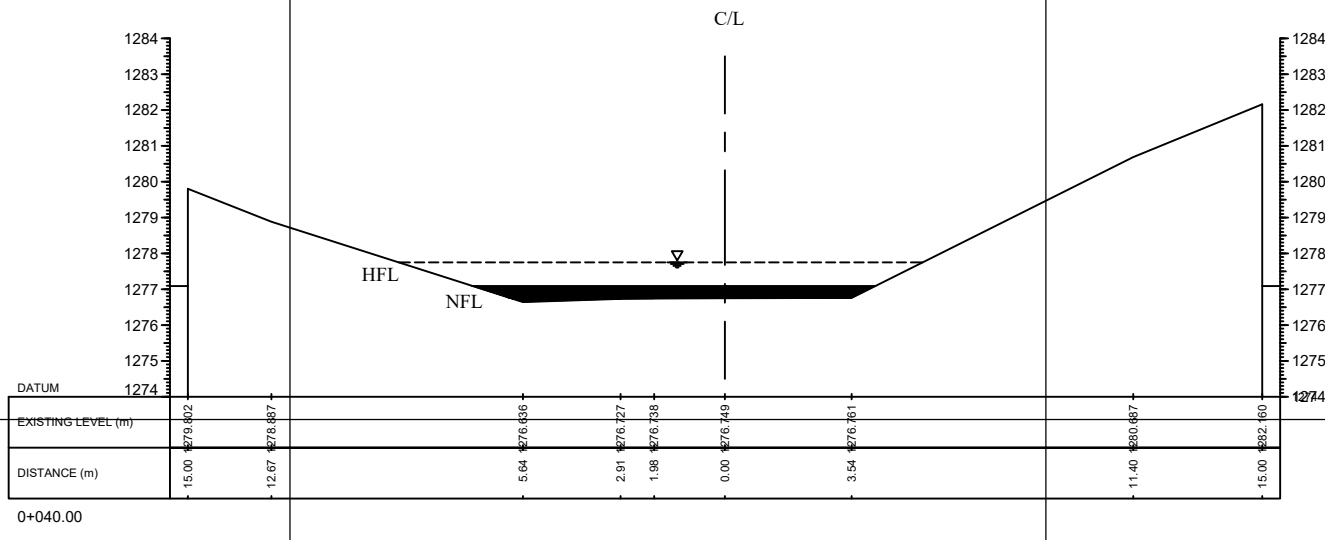
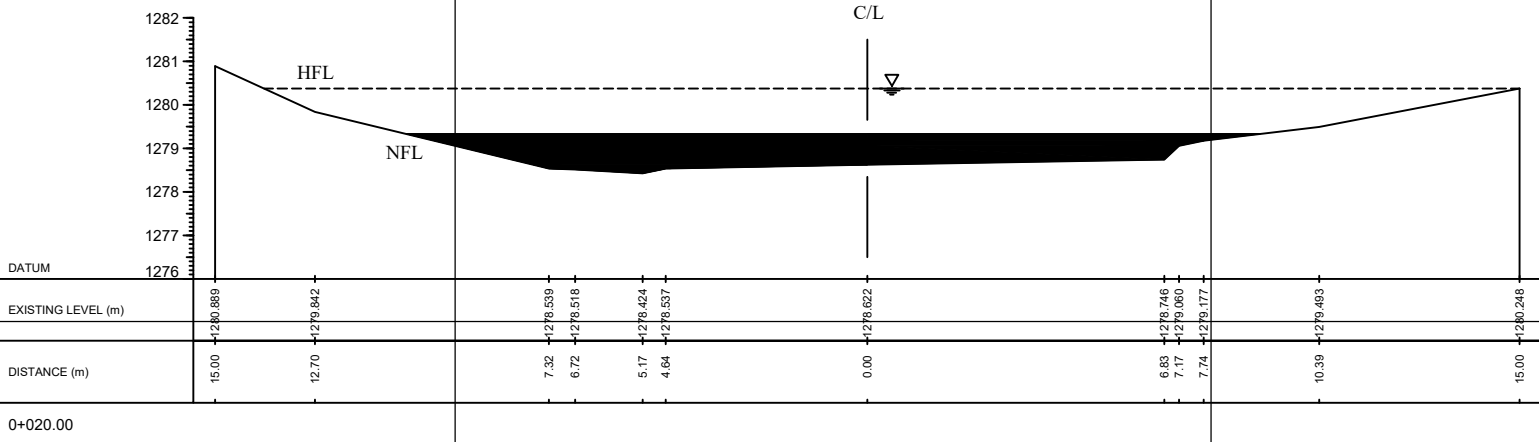
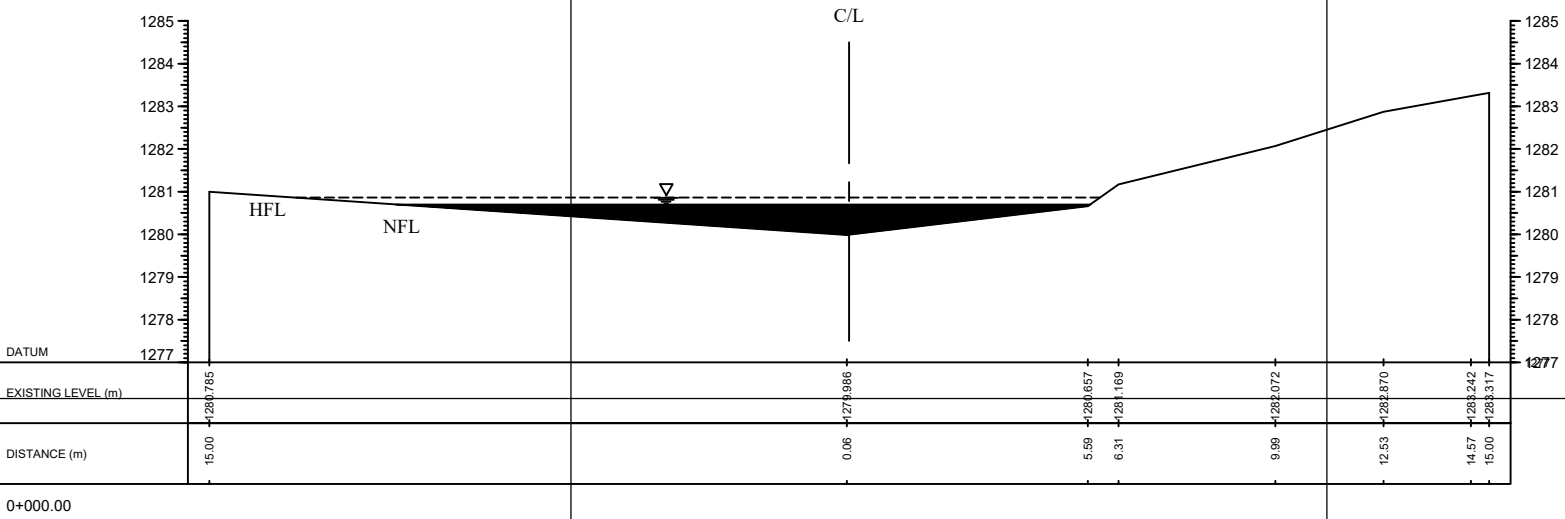


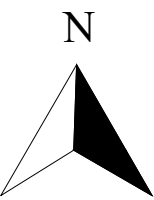

S.N.	LEGENDS	SYMBOL
1	NFL	————
2	HFL	-----
3	WATER LEVEL	▽
4	GROUND	~~~~~
5	AXIS LINE	

LOCATION: MARS NEPAL ENGINEERING
SURVEY CAMP, BUNGAMATI, LALITPUR

BRIDGE SURVEYING
CROSS SECTION

SUBMITTED BY: GROUP 7
SAMBHAV BELBASE (5)
NILESH JHA (16)
NISHAN LUITEL (21)
ANSHU RAJ OLI (30)
SWAPNIL REGMI (38)
BIBEK KUMAR SHAH (40)

SUBMITTED TO:
DEPARTMENT OF CIVIL ENGINEERING

SCALE: 1:3500
SHEET NO: 2
DATE OF SUBMISSION: 2023/09/27

