


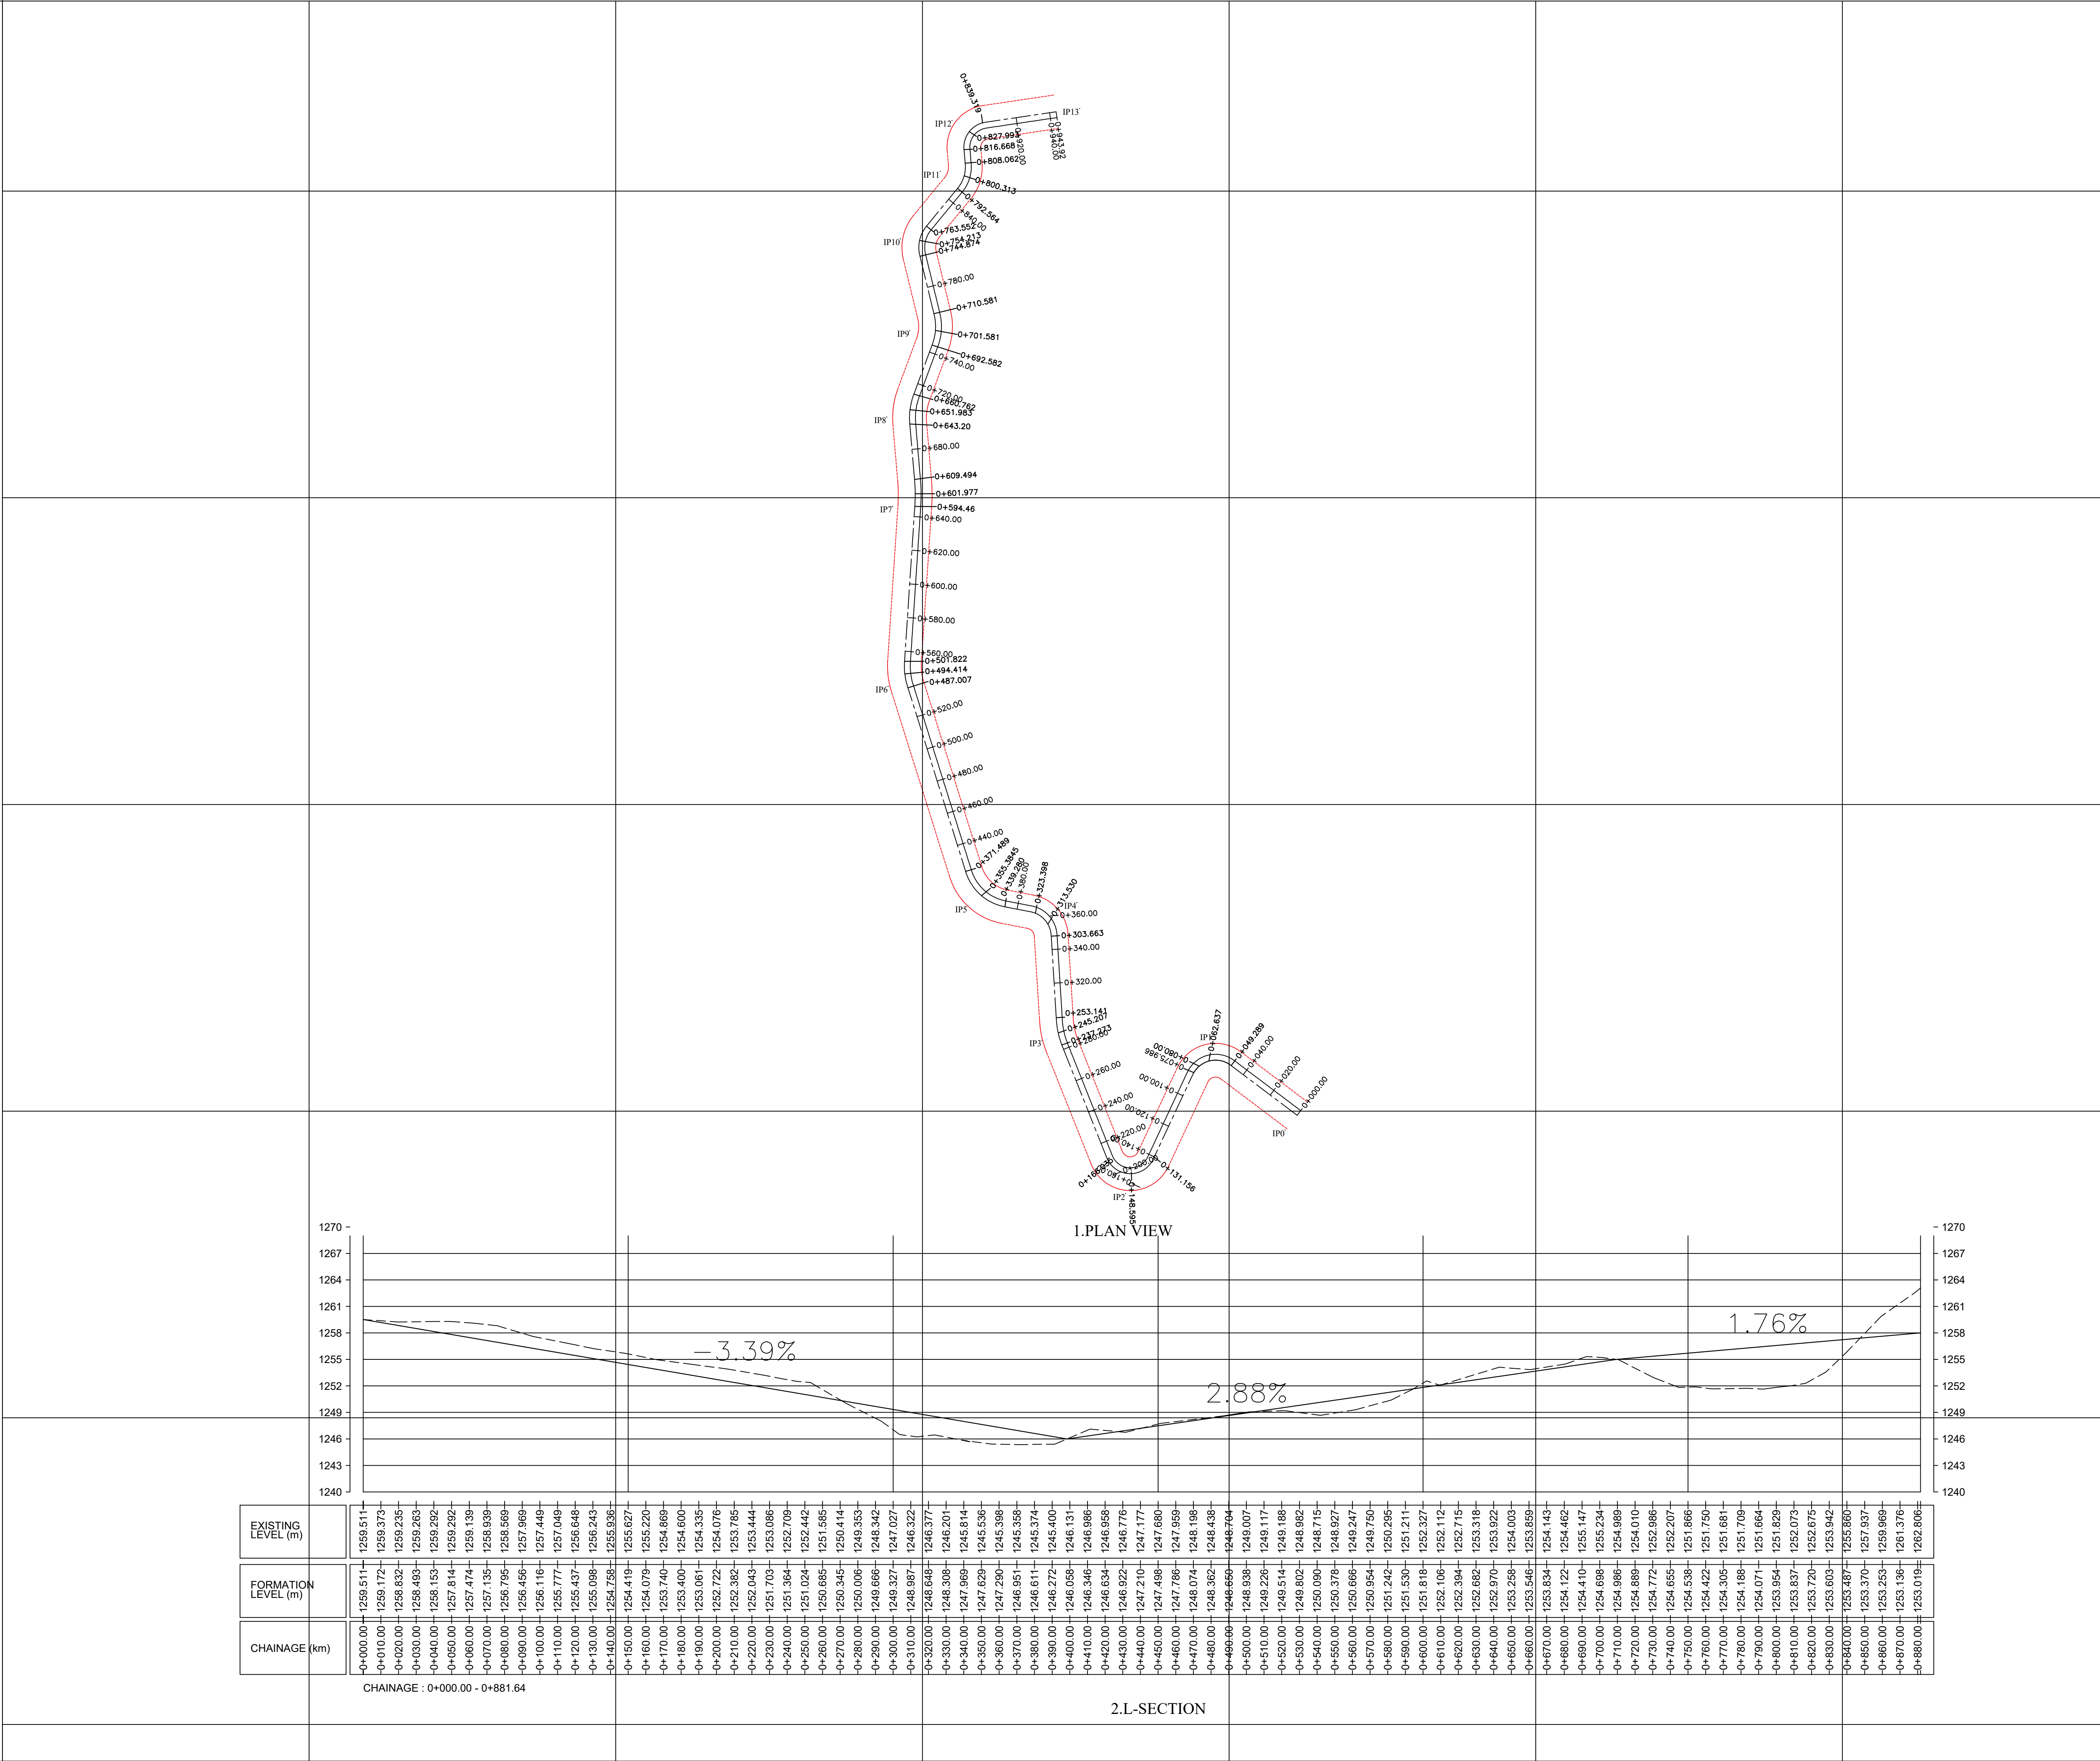

N

S.N.

LEGENDS

SYMBOL

1

CENTERLINE

2

ROAD

3

GROUND

4

RIGHT OF WAY

5

BOX CULVERT

6

STREAM

SN

NORTHING

EASTING

RADIUS

IP₀

1000.000

2000.000

IP₁

1040.803

1945.853

15

IP₂

942.634

1899.995

15

IP₃

1048.434

1857.784

50

IP₄

1118.416

1853.419

15

IP₅

1127.108

1808.940

30

IP₆

1261.495

1766.731

40

IP₇

1368.861

1773.826

100

IP₈

1418.845

1769.574

40

IP₉

1465.753

1786.941

30

IP₁₀

1519.405

1773.911

20

IP₁₁

1555.895

1803.934

20

IP₁₂

1586.660

1801.271

15

IP₁₃

1594.939

1857.090

LOCATION: FAST TRACK

BUNGAMATI, LALITPUR

TITLE: ROAD SURVEYING

PLAN VIEW AND L-SECTION

SUBMITTED BY: GROUP 7

SAMBHAV BELBAESE(05)

NILESH JHA (16)

NISHAN LUITEL (21)

ANSHU RAJ OLI (30)

SWAPNIL REGMI (38)

BIBEK KUMAR SHAH (40)

SUBMITTED TO:

DEPARTMENT OF CIVIL ENGINEERING

KATHMANDU UNIVERSITY

1.SCALE: 1:800

0

8

40

80m

2.SCALE: 1:700

0

7

35

70m

SHEET NO: 1

DATE OF SUBMISSION: 2023/09/26