


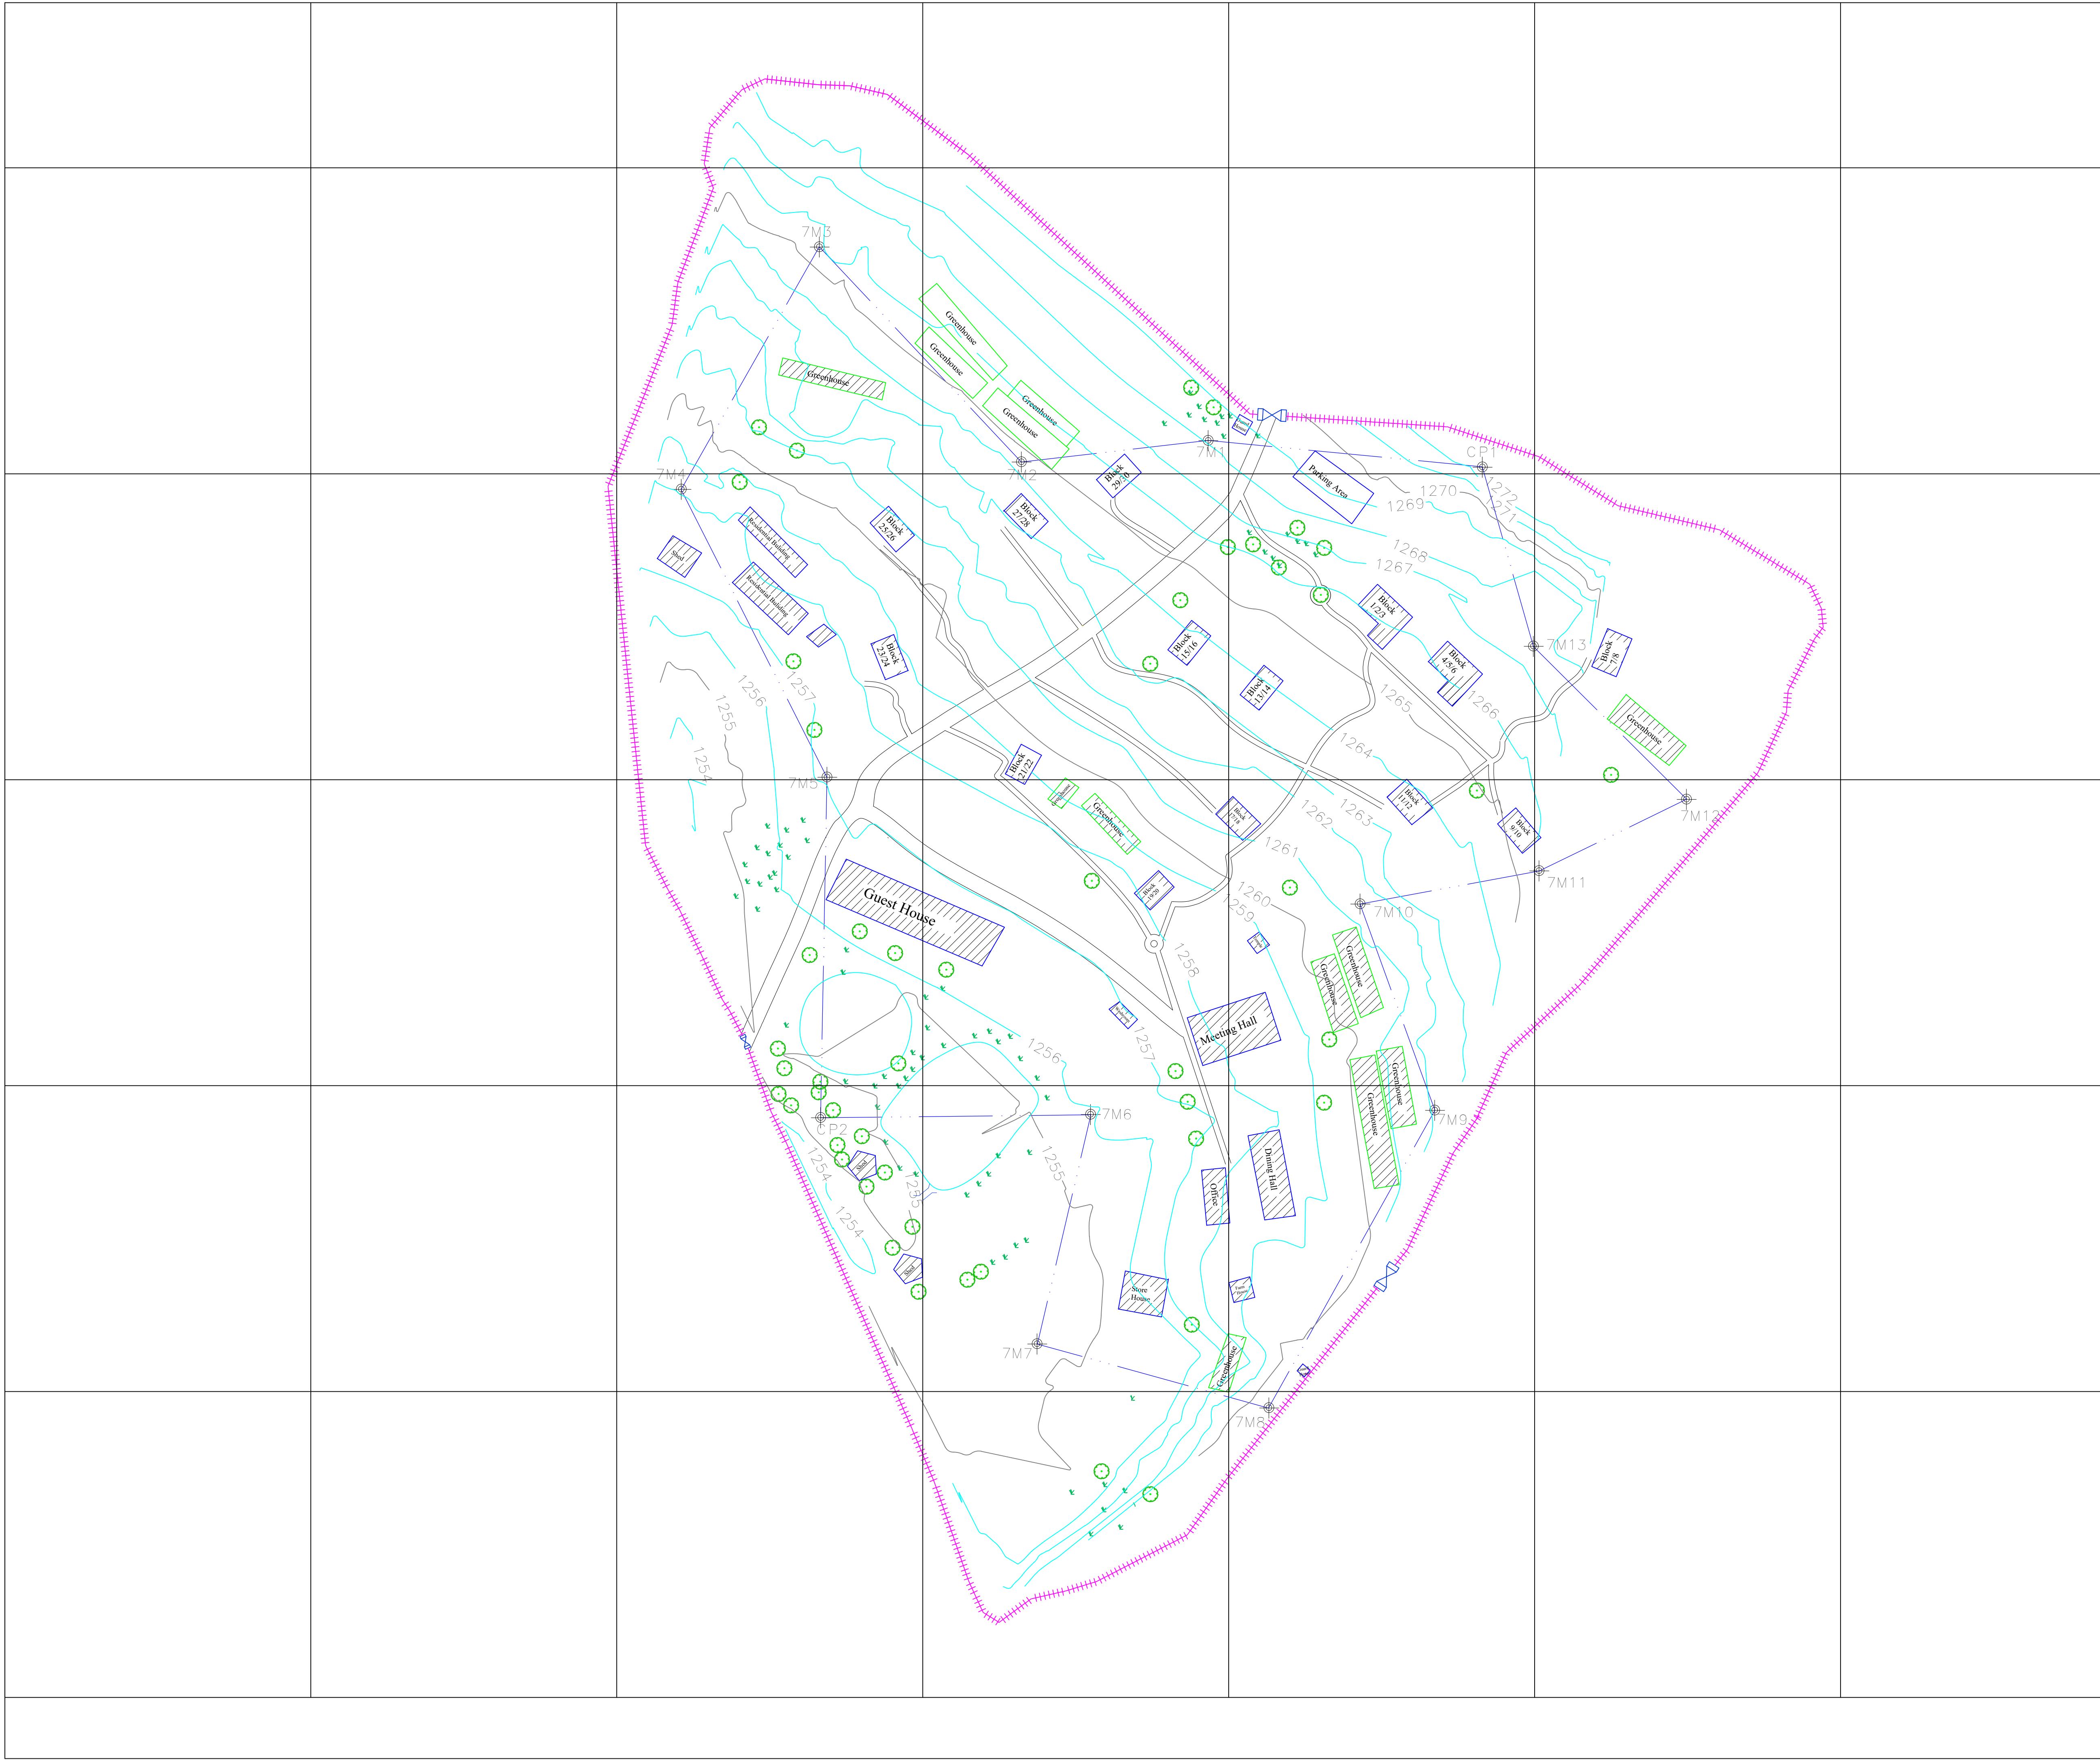

N			
SN	NORTHING(m)	EASTING(m)	RL(m)
CP1	3055749.000	331855.000	1272.756
7M1	3055754.169	331801.219	1269.214
7M2	3055749.939	331764.601	1264.814
7M3	3055792.159	331724.983	1266.098
7M4	3055744.522	331697.879	1258.409
7M5	3055688.099	331726.476	1257.454
CP2	3055621.326	331725.226	1255.901
7M6	3055621.915	331778.226	1256.089
7M7	3055576.952	331767.756	1254.331
7M8	3055564.397	331813.066	1260.519
7M9	3055622.804	331845.693	1261.102
7M10	3055663.256	331831.018	1261.216
7M11	3055669.723	331866.134	1265.433
7M12	3055683.816	331895.088	1267.74
7M13	3055713.736	331865.022	1268.165
S.N.	LEGENDS		SYMBOL
1	TREE		
2	BUILDING		
3	ELECTRIC POLE		
4	MAJOR TRAVERSE		
5	POND		
6	WATER TANK		
7	SHED		
8	ROAD		
9	TRAVERSE LEG		
10	FENCE		
11	FENCE GATE		
LOCATION: MARS NEPAL ENGINEERING			
SURVEY CAMP, BUNGAMATI, LALITPUR			
TOPOGRAPHICAL MAP			
PREPARED BY: GROUP 7			
SAMBHAV BELBASE(5)			
NILESH KUMAR JHA(16)			
NISHAN LUITEL (21)			
ANSHU RAJ OLI (30)			
SWAPNIL REGMI (38)			
BIBEK KUMAR SHAH (40)			
SUBMITTED TO:			
DEPARTMENT OF CIVIL ENGINEERING			
SCALE: 1:600			
SHEET NO: 1			
DATE OF SUBMISSION: 2023/09/24			
GRAPHICAL SCALE			